
Wand A – Spülenzeile (Fensterwand)

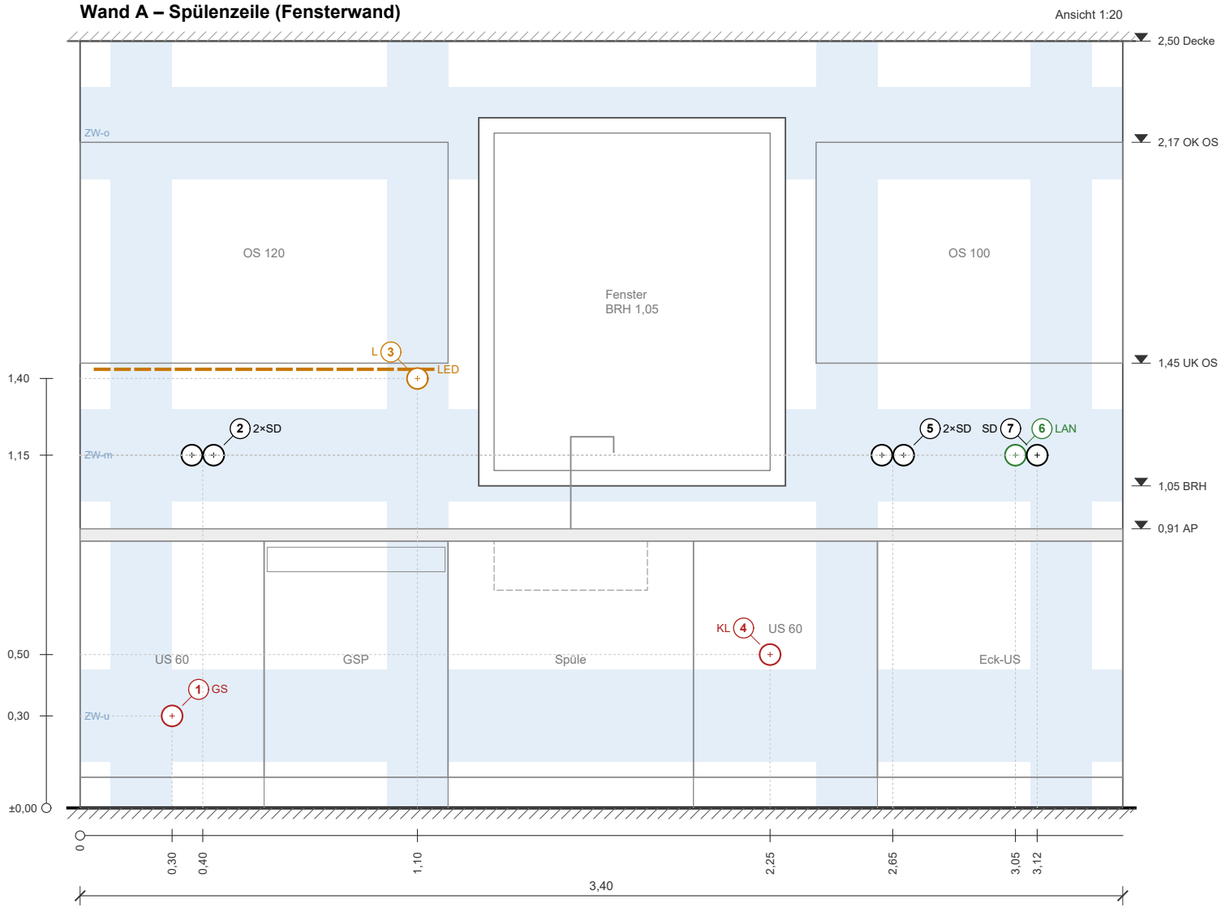

Elektropunkte

Nr.	Symbol	Bezeichnung	x	h	SK	Bemerkung
1	GS	Geräteanschluss Geschirrspüler Wand A	0,30	0,30	**F6**	im Nachbarschrank, nicht hinter dem GSP
2	2	Steckdose 2-fach – Arbeitsplatte Wand A	0,40	1,15	**F3**	
3		Leuchtenauslass – Unterbauleuchte Wand A	1,10	1,40	**F2**	Leitung 30 cm Vorrat, Treiber im OS
4	KL	Geräteanschluss Kleinspeicher / Untertis… Wand A	2,25	0,50	**F7**	Untertischgerät 5 l, Steckdose im Spülenschrank
5	2	Steckdose 2-fach – Arbeitsplatte Wand A	2,65	1,15	**F3**	
6	LAN	Datendose (IuK) – LAN Wand A	3,05	1,15		
7		Steckdose – IuK Wand A	3,12	1,15	**F3**	im 2-fach-Rahmen mit Pkt. 6

Farben


- Steckdose
- Geräteanschluss (eigener Stromkreis)
- Daten / TV / Telefon
- Schalter / Taster / Dimmer
- Leuchtenauslass
- Dose / Melder / Sonstiges

Installationszonen DIN 18015-3 (ZW-u/-m/-o waagerecht, ZS senkrecht)

Maße in m. x = Dosenmitte ab linker Wandecke (fertige Wand), h = Dosenmitte über OKFF.
Mehrfachkombination: x = Mitte, h = Dosenmitte; * = senkrecht, h = oberste Dose.
Dosen maßstäblich Ø 68 mm, Raster 71 mm. Höhen über Meterriss prüfen (Meterriss = OKFF + 1,00 m).
Möbelmaße (AP 0,91, UK OS 1,45) aus der Küchenplanung übernehmen und vor dem Schlitzen mit dem Küchenbauer abstimmen.
Geräteanschlüsse nach Herstellerangabe (Einbauanleitung) – Lage hinter/neben dem Gerät.

MUSTER Elektrotechnik	Muster Elektrotechnik GmbH	Elektroplan Küche – Wandansichten (1/3)	Kunde	Familie Muster	Blatt
	Max Mustermann · Musterstraße 1		Objekt	Musterstraße 12, 12345 Musterstadt	1/3
	12345 Musterstadt	Küche · Maßstab 1:20	Auftrag	2026-014	
	Tel. 0123 456789 · muster-elektro.de	Wandansicht · Höhen über OKFF · Symbole DIN EN 60617-11	Erstellt	12.10.2026 · M. Mustermann	Rev. A

Wand B – Herdzeile mit Hochschränken

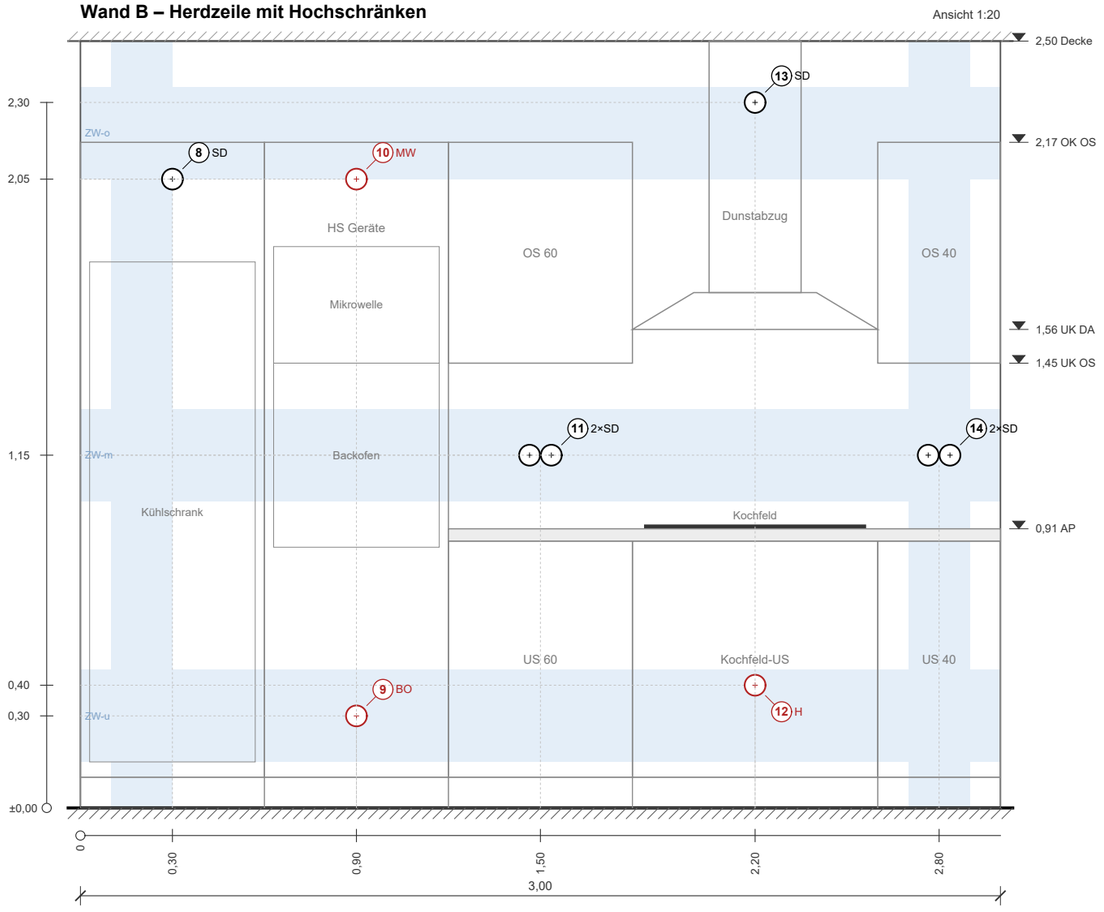

Elektropunkte

Nr.	Symbol	Bezeichnung	x	h	SK	Bemerkung
8		Steckdose – Kühlschrank Wand B	0,30	2,05	**F8**	über dem Gerät im HS-Oberteil
9	BO	Geräteanschluss Backofen Wand B	0,90	0,30	**F9**	im Sockelfach des Geräte-HS
10	MW	Geräteanschluss Mikrowelle Wand B	0,90	2,05	**F11**	Kombi-Mikrowelle
11	2	Steckdose 2-fach – Arbeitsplatte Wand B	1,50	1,15	**F4**	
12	H	Geräteanschluss Herd/Kochfeld (3 × 230 V) Wand B	2,20	0,40	**F10**	Herdanschlussdose, 5×2,5 mm²
13		Steckdose – Dunstabzug Wand B	2,20	2,30	**F4**	in der Kaminverkleidung
14	2	Steckdose 2-fach – Arbeitsplatte Wand B	2,80	1,15	**F4**	

Farben

- Steckdose
- Geräteanschluss (eigener Stromkreis)
- Daten / TV / Telefon
- Schalter / Taster / Dimmer
- Leuchtenauslass
- Dose / Melder / Sonstiges


Installationszonen DIN 18015-3 (ZW-u/-m/-o waagerecht, ZS senkrecht)

Maße in m. x = Dosenmitte ab linker Wandecke (fertige Wand), h = Dosenmitte über OKFF.
Mehrfachkombination: x = Mitte, h = Dosenmitte; * = senkrecht, h = oberste Dose.
Dosen maßstäblich Ø 68 mm, Raster 71 mm. Höhen über Meterriss prüfen (Meterriss = OKFF + 1,00 m).
Möbelmaße (AP 0,91, UK OS 1,45) aus der Küchenplanung übernehmen und vor dem Schlitzen mit dem Küchenbauer abstimmen.
Geräteanschlüsse nach Herstellerangabe (Einbauanleitung) – Lage hinter/neben dem Gerät.

MUSTER Elektrotechnik	Muster Elektrotechnik GmbH	Elektroplan Küche – Wandansichten (2/3)	Kunde	Familie Muster	Blatt
	Max Mustermann · Musterstraße 1		Objekt	Musterstraße 12, 12345 Musterstadt	2/3
	12345 Musterstadt	Küche · Maßstab 1:20	Auftrag	2026-014	
	Tel. 0123 456789 · muster-elektro.de	Wandansicht · Höhen über OKFF · Symbole DIN EN 60617-11	Erstellt	12.10.2026 · M. Mustermann	Rev. A

Wand C – Türwand

Ansicht 1:20

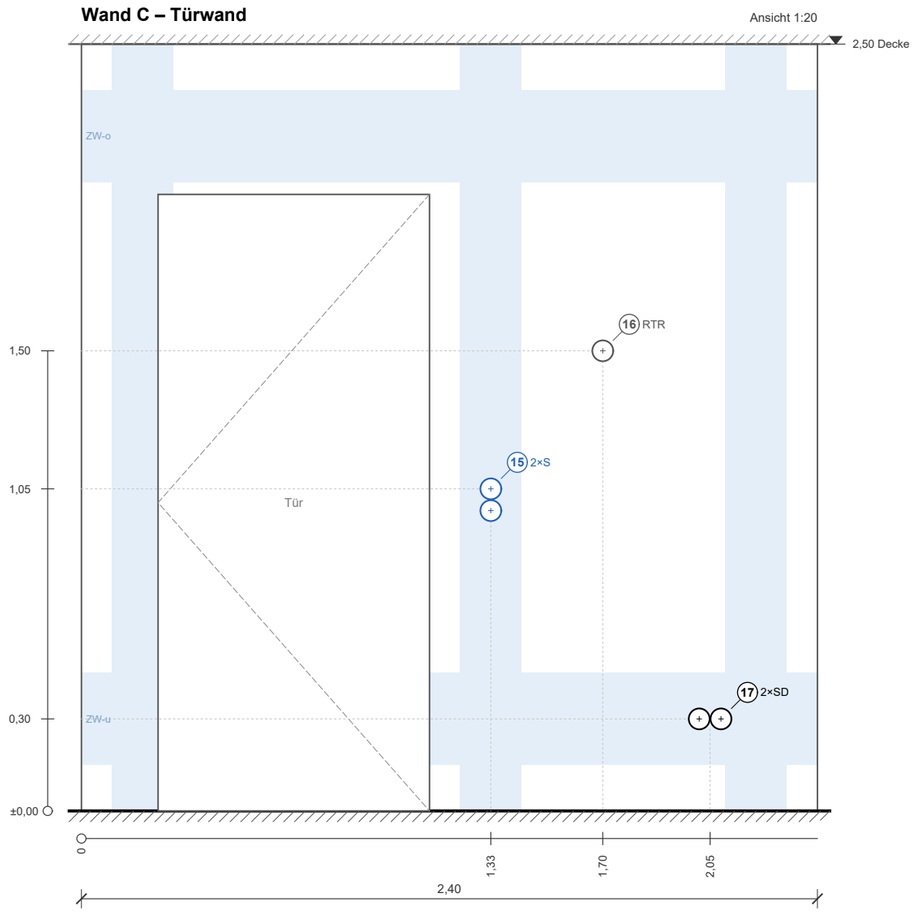

Elektropunkte

Nr.	Symbol	Bezeichnung	x	h	SK	Bemerkung
15		Ausschalter 2-fach – Decke / Unterbau Wand C	1,33	1,05*	**F2**	
16	RTR	Melder/Sensor RTR Wand C	1,70	1,50		Raumthermostat FBH, nach Hersteller
17	2	Steckdose 2-fach – allgemein Wand C	2,05	0,30	**F5**	

Farben

- Steckdose
- Geräteanschluss (eigener Stromkreis)
- Daten / TV / Telefon
- Schalter / Taster / Dimmer
- Leuchtenauslass
- Dose / Melder / Sonstiges

Installationszonen DIN 18015-3 (ZW-u/-m/-o waagerecht, ZS senkrecht)

Maße in m. x = Dosenmitte ab linker Wandecke (fertige Wand), h = Dosenmitte über OKFF.
Mehrfachkombination: x = Mitte, h = Dosenmitte; * = senkrecht, h = oberste Dose.
Dosen maßstäblich Ø 68 mm, Raster 71 mm. Höhen über Meterriss prüfen (Meterriss = OKFF + 1,00 m).
Möbelmaße (AP 0,91, UK OS 1,45) aus der Küchenplanung übernehmen und vor dem Schlitzen mit dem Küchenbauer abstimmen.
Geräteanschlüsse nach Herstellerangabe (Einbauanleitung) – Lage hinter/neben dem Gerät.

MUSTER Elektrotechnik	Muster Elektrotechnik GmbH	Elektroplan Küche – Wandansichten (3/3)	Kunde	Familie Muster	Blatt
	Max Mustermann · Musterstraße 1		Objekt	Musterstraße 12, 12345 Musterstadt	3/3
	12345 Musterstadt	Küche · Maßstab 1:20	Auftrag	2026-014	
	Tel. 0123 456789 · muster-elektro.de	Wandansicht · Höhen über OKFF · Symbole DIN EN 60617-11	Erstellt	12.10.2026 · M. Mustermann	Rev. A