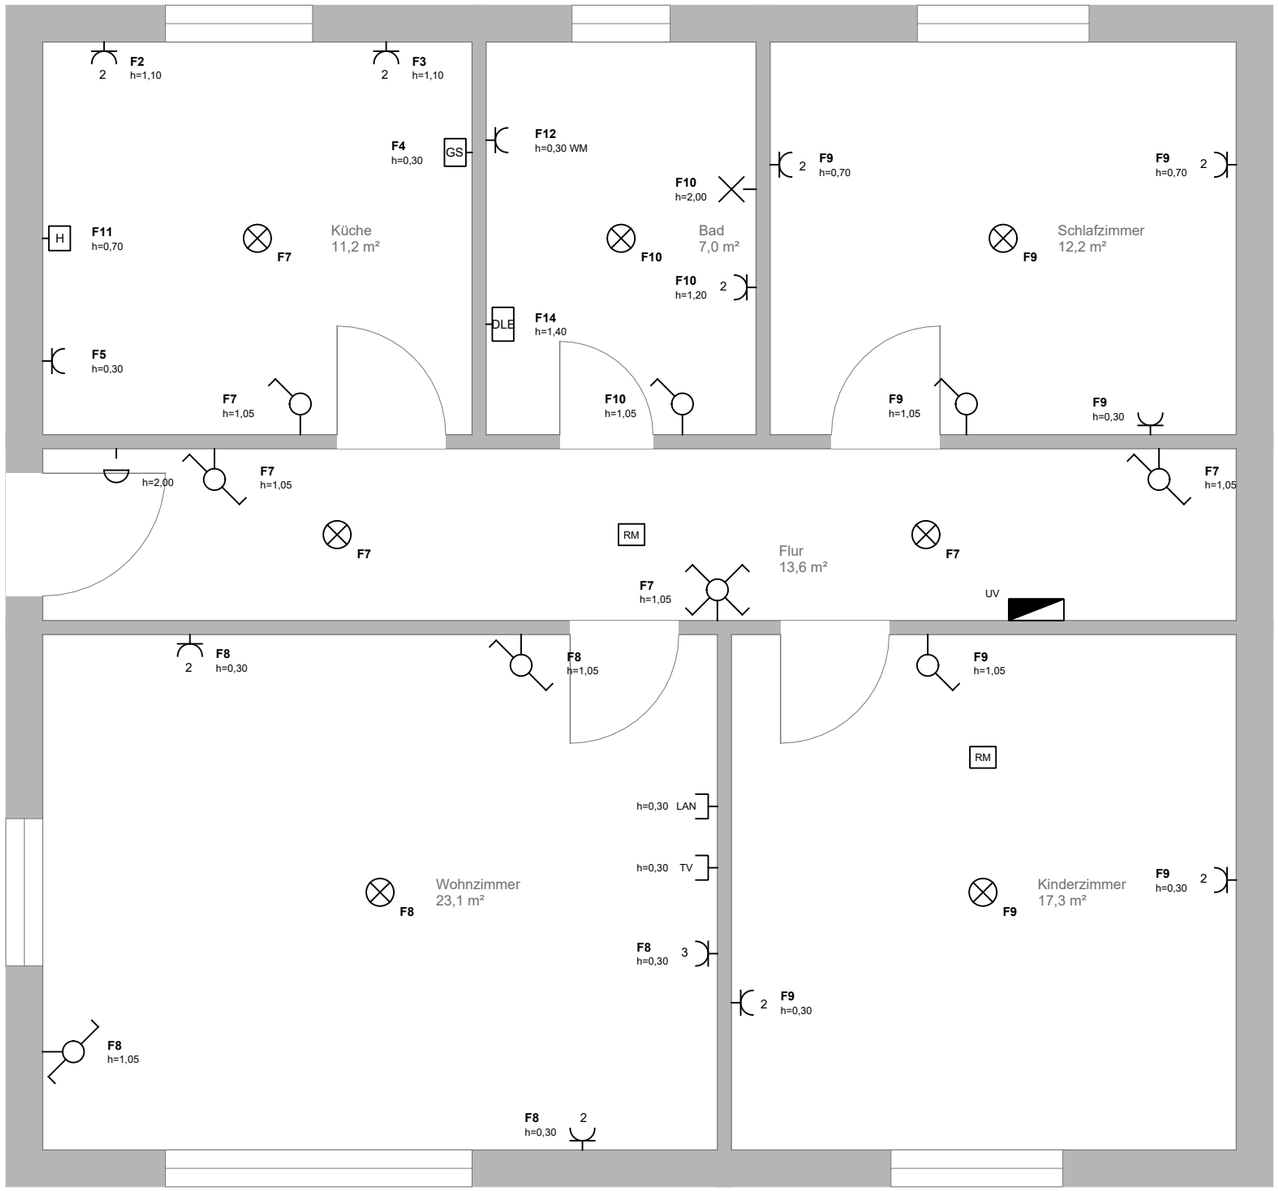


Legende

	Stromkreisverteiler	1×
	Schutzkontaktsteckdose	3×
2	2-fach-Schutzkontaktsteckdose	9×
3	3-fach-Schutzkontaktsteckdose	1×
DLE	Geräteanschluss DLE	1×
GS	Geräteanschluss GS	1×
H	Geräteanschluss H	1×
LAN	Fernmelde-/Datensteckdose LAN	1×
TV	Fernmelde-/Datensteckdose TV	1×
	Ausschalter	4×
	Kreuzschalter	1×
	Wechselschalter	4×
	Leuchte (Deckenauslass)	7×
	Wandleuchte (Wandauslass)	1×
RM	Melder/Sensor RM	2×
	Klingel / Gong	1×

Beschriftung am Symbol: Stromkreis (z. B. F3), h = Montagehöhe über OKFF in m

Maßstab 1:50 (bei Druck in Originalgröße)

0 0,5 1 1,5 2 2,5 m

MUSTER Elektrotechnik	Muster Elektrotechnik GmbH	Installationsplan Wohnung 1. OG	Kunde	Familie Muster	Blatt
	Max Mustermann · Musterstraße 1		Objekt	Musterstraße 12, 12345 Musterstadt	1/1
	12345 Musterstadt	Maßstab 1:50	Auftrag	2026-014	
	Tel. 0123 456789 · muster-elektro.de	Installationsplan · Symbole nach DIN EN 60617-11	Erstellt	08.10.2026 · M. Mustermann	Rev. A