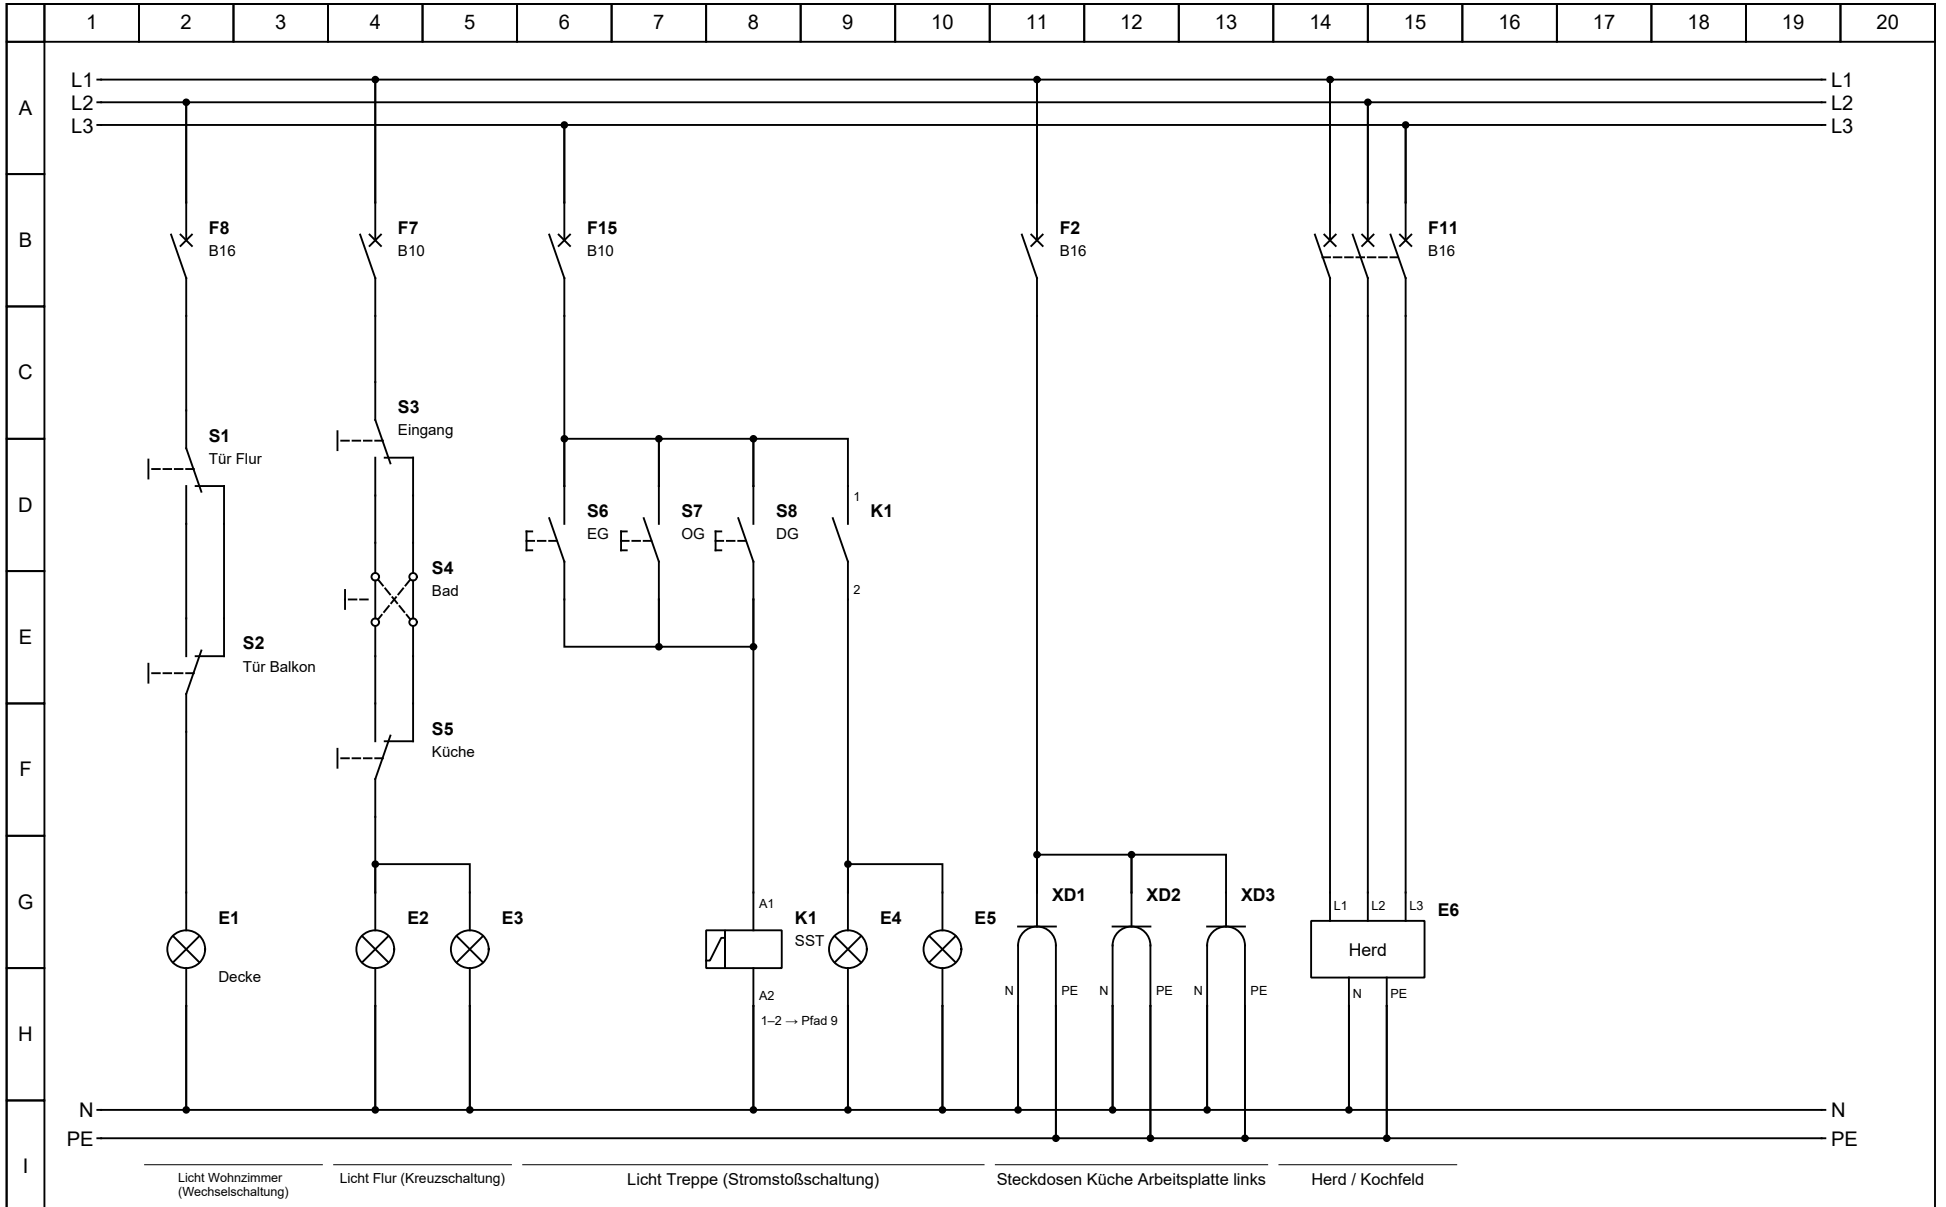


MUSTER Elektrotechnik	Muster Elektrotechnik GmbH	Stromlaufplan Beleuchtung und Steckdosen	Kunde	Familie Muster	Blatt
	Max Mustermann · Musterstraße 1		Objekt	Musterstraße 12, 12345 Musterstadt	1/1
	12345 Musterstadt	UV Wohnung 1. OG · Flur, Wohnzimmer, Küche	Auftrag	2026-014	
	Tel. 0123 456789 · muster-elektro.de	Stromlaufplan in aufgelöster Darstellung · DIN EN 61082 / DIN EN 60617	Erstellt	08.10.2026 · M. Mustermann	Rev. A