
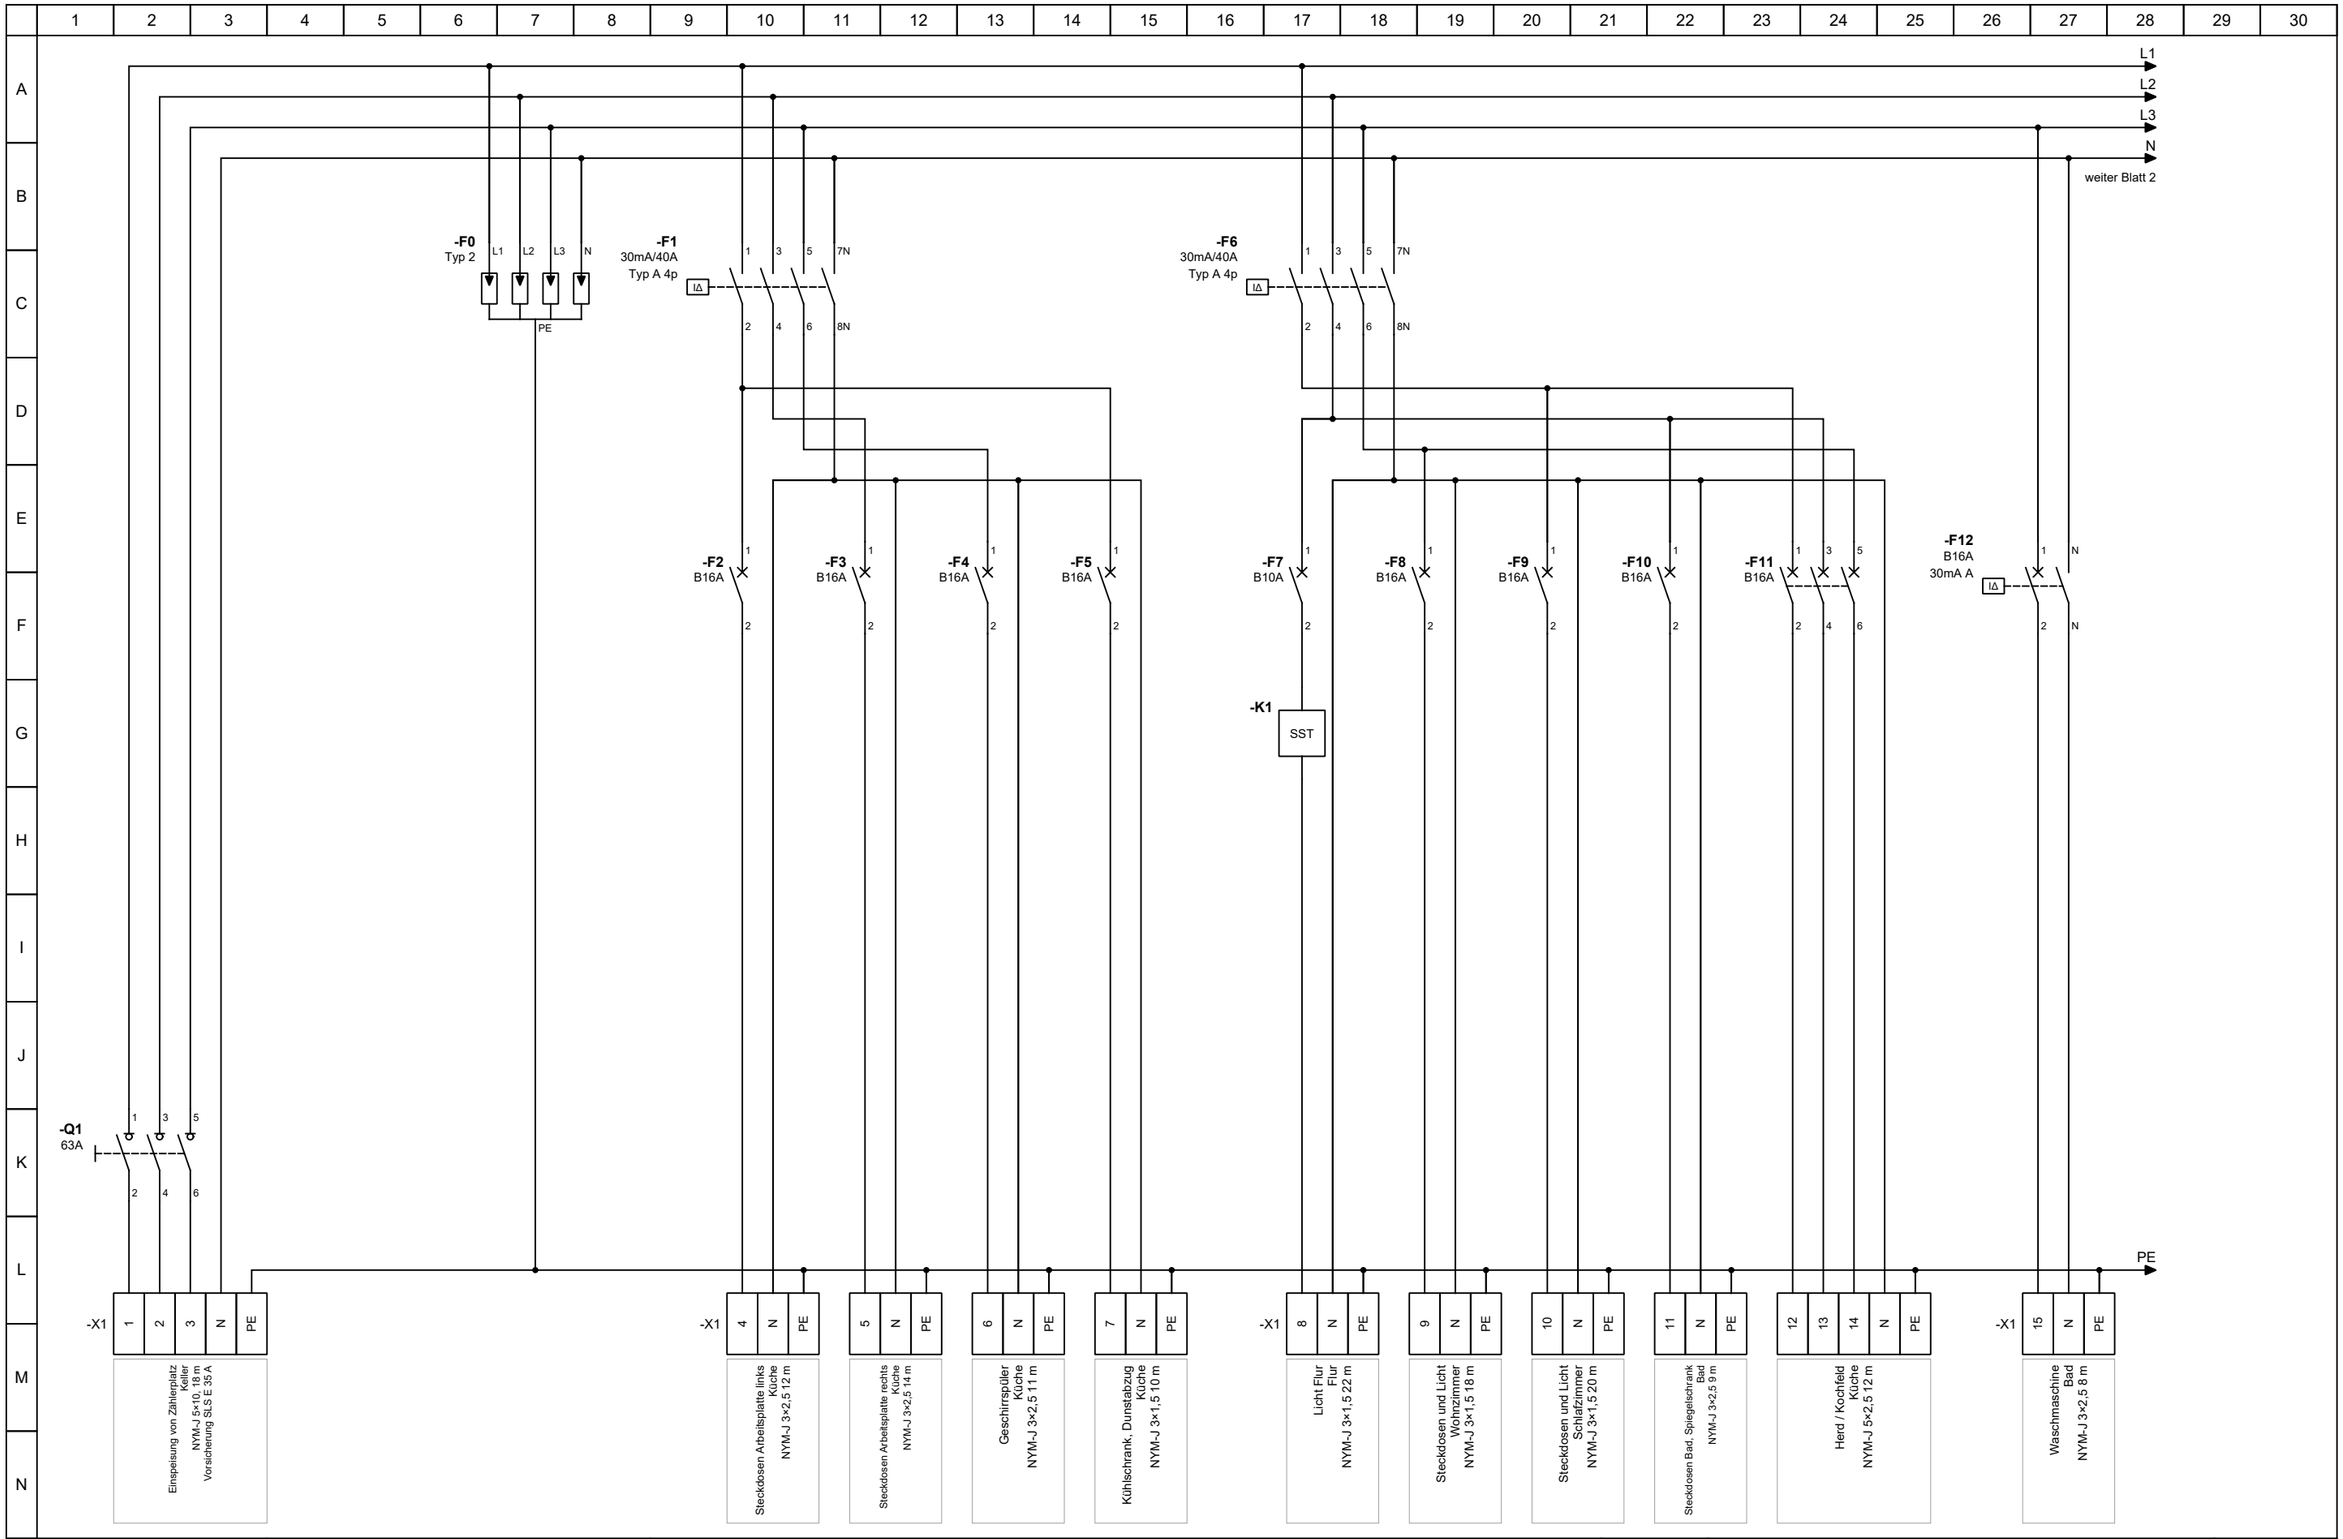


MUSTER Elektrotechnik	Muster Elektrotechnik GmbH Max Mustermann · Musterstraße 1 12345 Musterstadt Tel. 0123 456789 · muster-elektro.de	Stromlaufplan UV Wohnung 1. OG UV Wohnung 1. OG · Standort: Flur · Netz: TN-C-S Stromlaufplan Verteilung · allpolige Darstellung · DIN EN 61082 / DIN EN 60617	Kunde Objekt Auftrag Erstellt	Familie Muster Musterstraße 12, 12345 Musterstadt 2026-014 08.10.2026 · M. Mustermann	Blatt 1/2 Rev. A

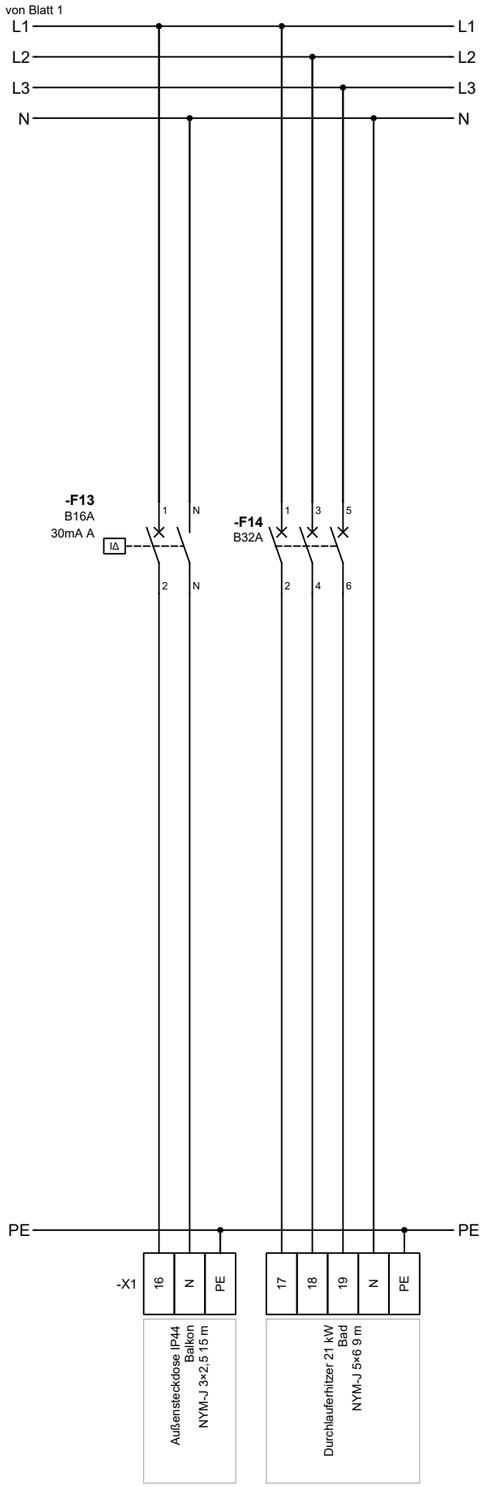

MUSTER Elektrotechnik	Muster Elektrotechnik GmbH	Stromlaufplan UV Wohnung 1. OG	Kunde	Familie Muster	Blatt
	Max Mustermann · Musterstraße 1		Objekt	Musterstraße 12, 12345 Musterstadt	2/2
	12345 Musterstadt	UV Wohnung 1. OG · Standort: Flur · Netz: TN-C-S	Auftrag	2026-014	
	Tel. 0123 456789 · muster-elektro.de	Stromlaufplan Verteilung · allpolige Darstellung · DIN EN 61082 / DIN EN 60617	Erstellt	08.10.2026 · M. Mustermann	Rev. A