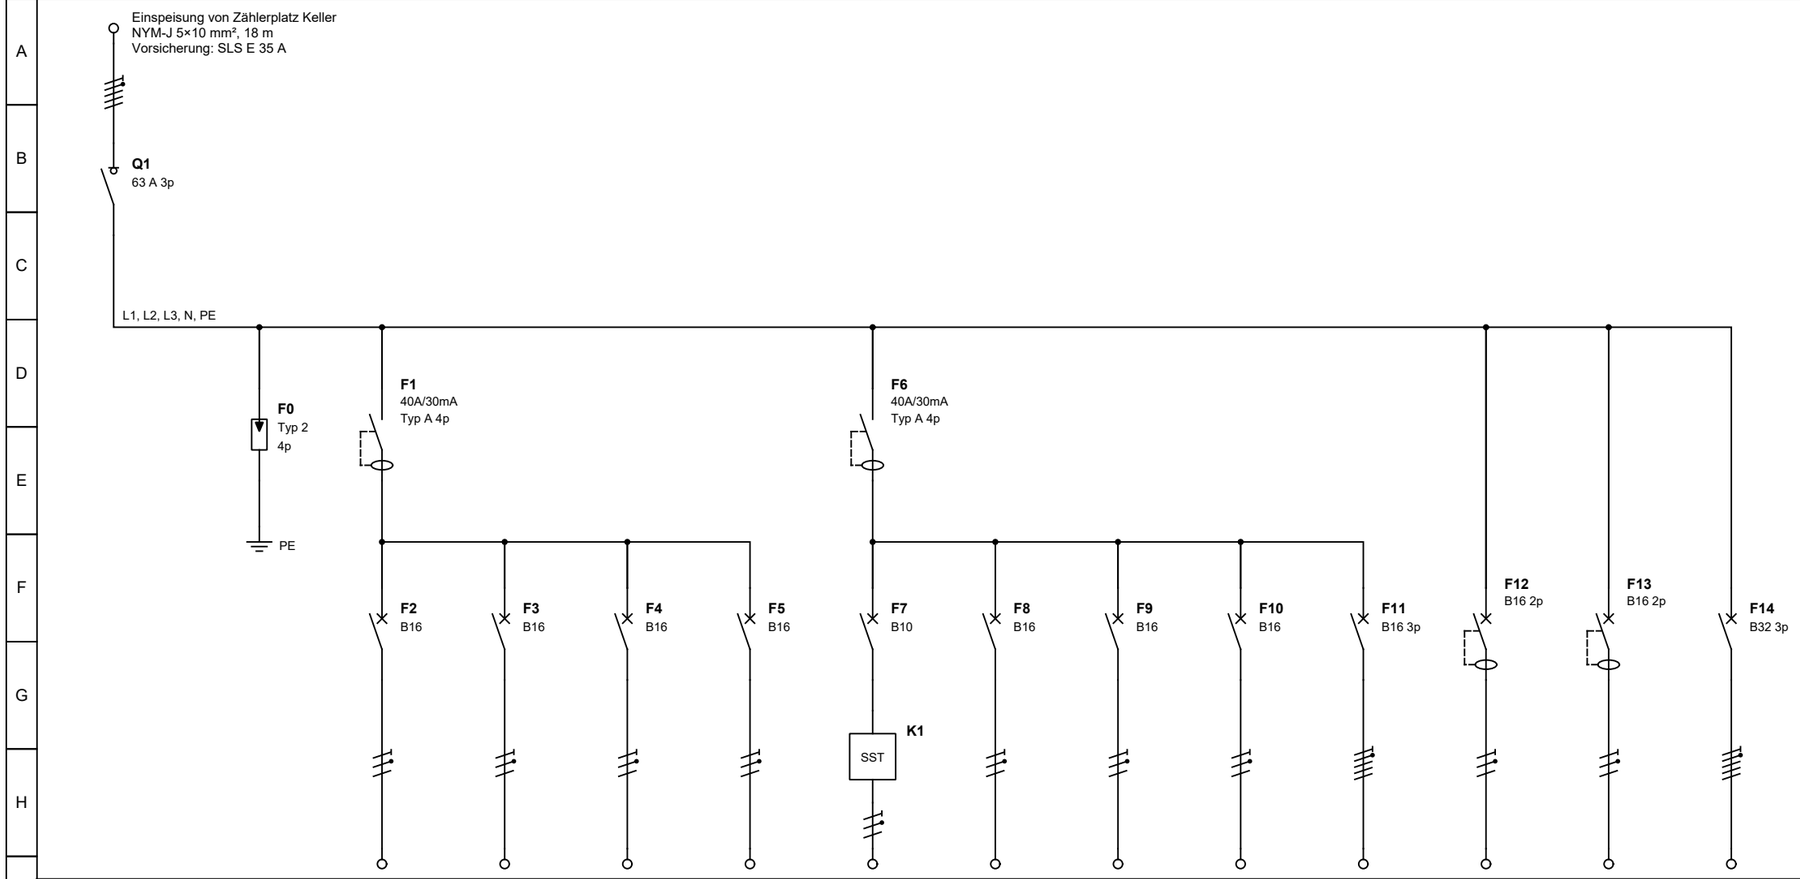


BMK	F0	F2	F3	F4	F5	F7	F8	F9	F10	F11	F12	F13	F14
Schutzorgan	Typ 2	B16	B16	B16	B16	B10	B16	B16	B16	B16 3p	B16 2p	B16 2p	B32 3p
FI-Schutz	–	F1	F1	F1	F1	F6	F6	F6	F6	F6	30 mA	30 mA	–
Phase	L1–L3	L1	L2	L3	L1	L2	L3	L1	L2	L1–L3	L3	L1	L1–L3
Leitung / Länge		NYM-J 3×2,5 12 m	NYM-J 3×2,5 14 m	NYM-J 3×2,5 11 m	NYM-J 3×1,5 10 m	NYM-J 3×1,5 22 m	NYM-J 3×1,5 18 m	NYM-J 3×1,5 20 m	NYM-J 3×2,5 9 m	NYM-J 5×2,5 12 m	NYM-J 3×2,5 8 m	NYM-J 3×2,5 15 m	NYM-J 5×6 9 m
Verbraucher / Raum	Überspannungsschutz	Steckdosen Arbeitsplatte links Küche	Steckdosen Arbeitsplatte rechts Küche	Geschirrspüler Küche	Kühlschrank, Dunstabzug Küche	Licht Flur Flur	Steckdosen und Licht Wohnzimmer	Steckdosen und Licht Schlafzimmer	Steckdosen Bad, Spiegelschrank Bad	Herd / Kochfeld Küche	Waschmaschine Bad	Außensteckdose IP44 Balkon	Durchlauferhitzer 21 kW Bad

MUSTER Elektrotechnik	Muster Elektrotechnik GmbH	Verteilerplan UV Wohnung 1. OG	Kunde: Familie Muster · Blatt: 1/1
	Max Mustermann · Musterstraße 1		Objekt: Musterstraße 12, 12345 Musterstadt
	12345 Musterstadt	UV Wohnung 1. OG · Standort: Flur · Netz: TN-C-S	Auftrag: 2026-014
	Tel. 0123 456789 · muster-elektro.de	Übersichtsschaltplan · einpolige Darstellung nach DIN EN 60617	Erstellt: 08.10.2026 · M. Mustermann · Rev. A